


MILOKAHA 1.1

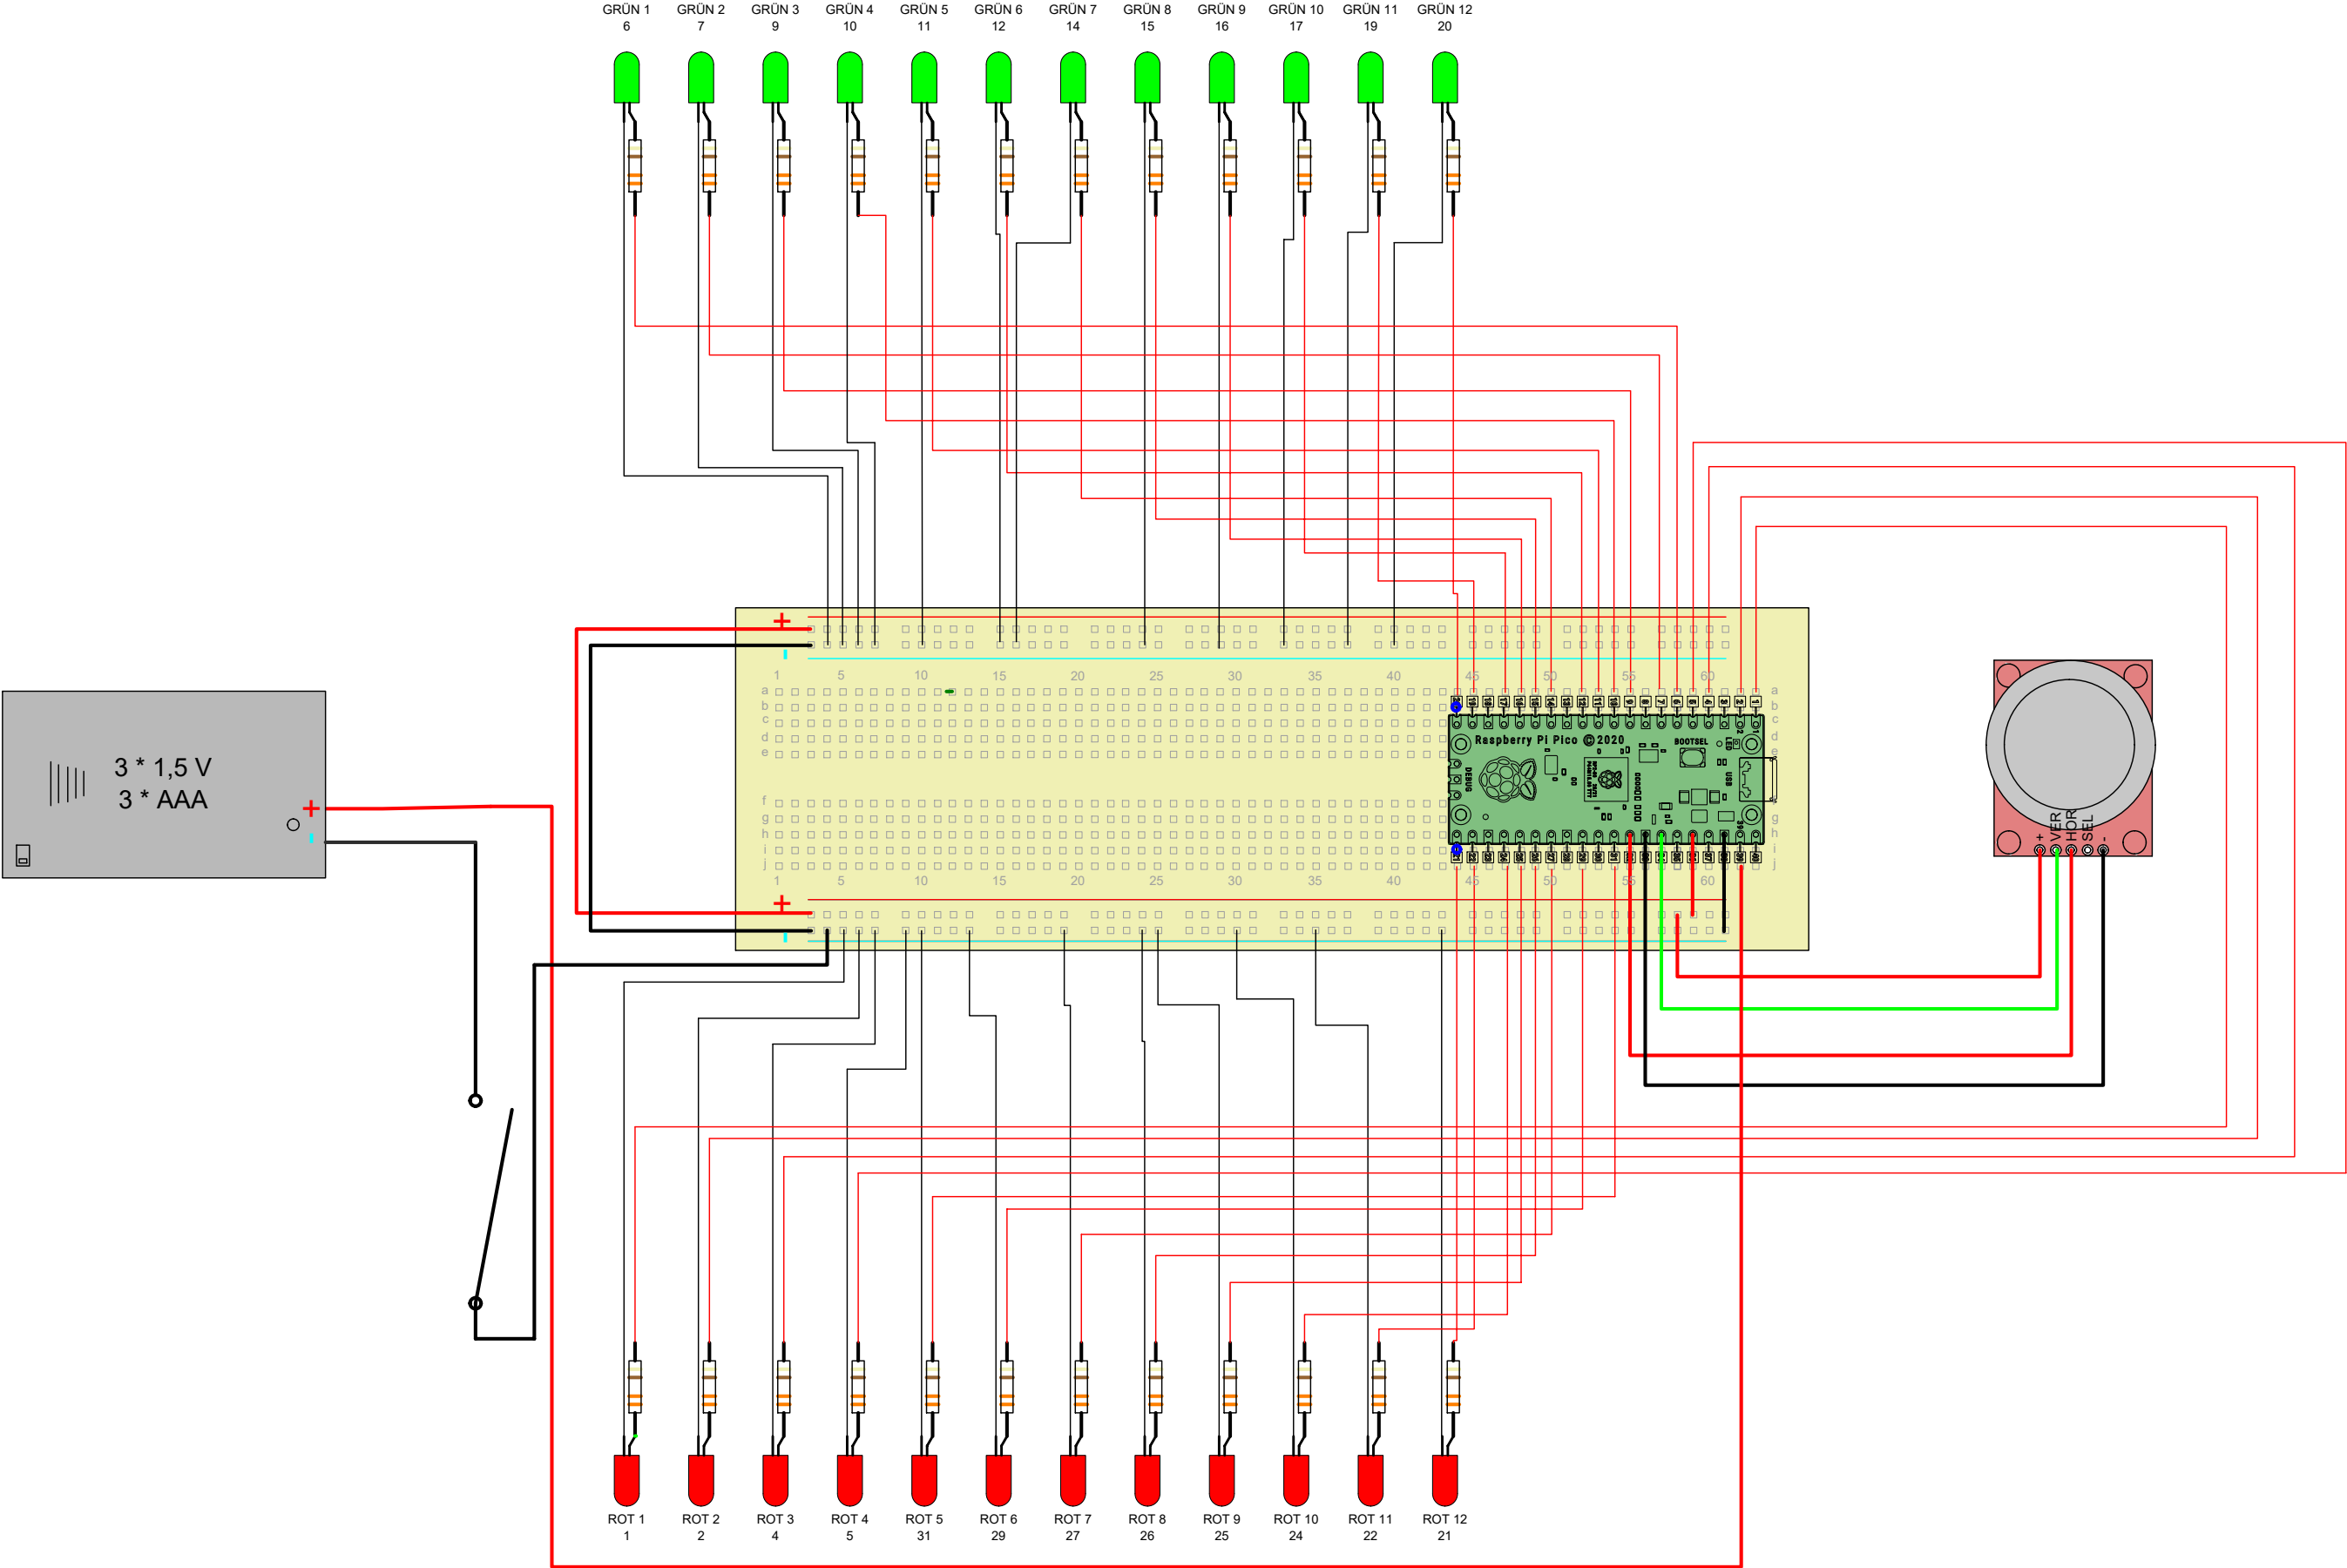

Schaltplan LEDs mit vorgelöteten Widerständen